



LOCATION: LILONGWE NANJIRI SITE 1A

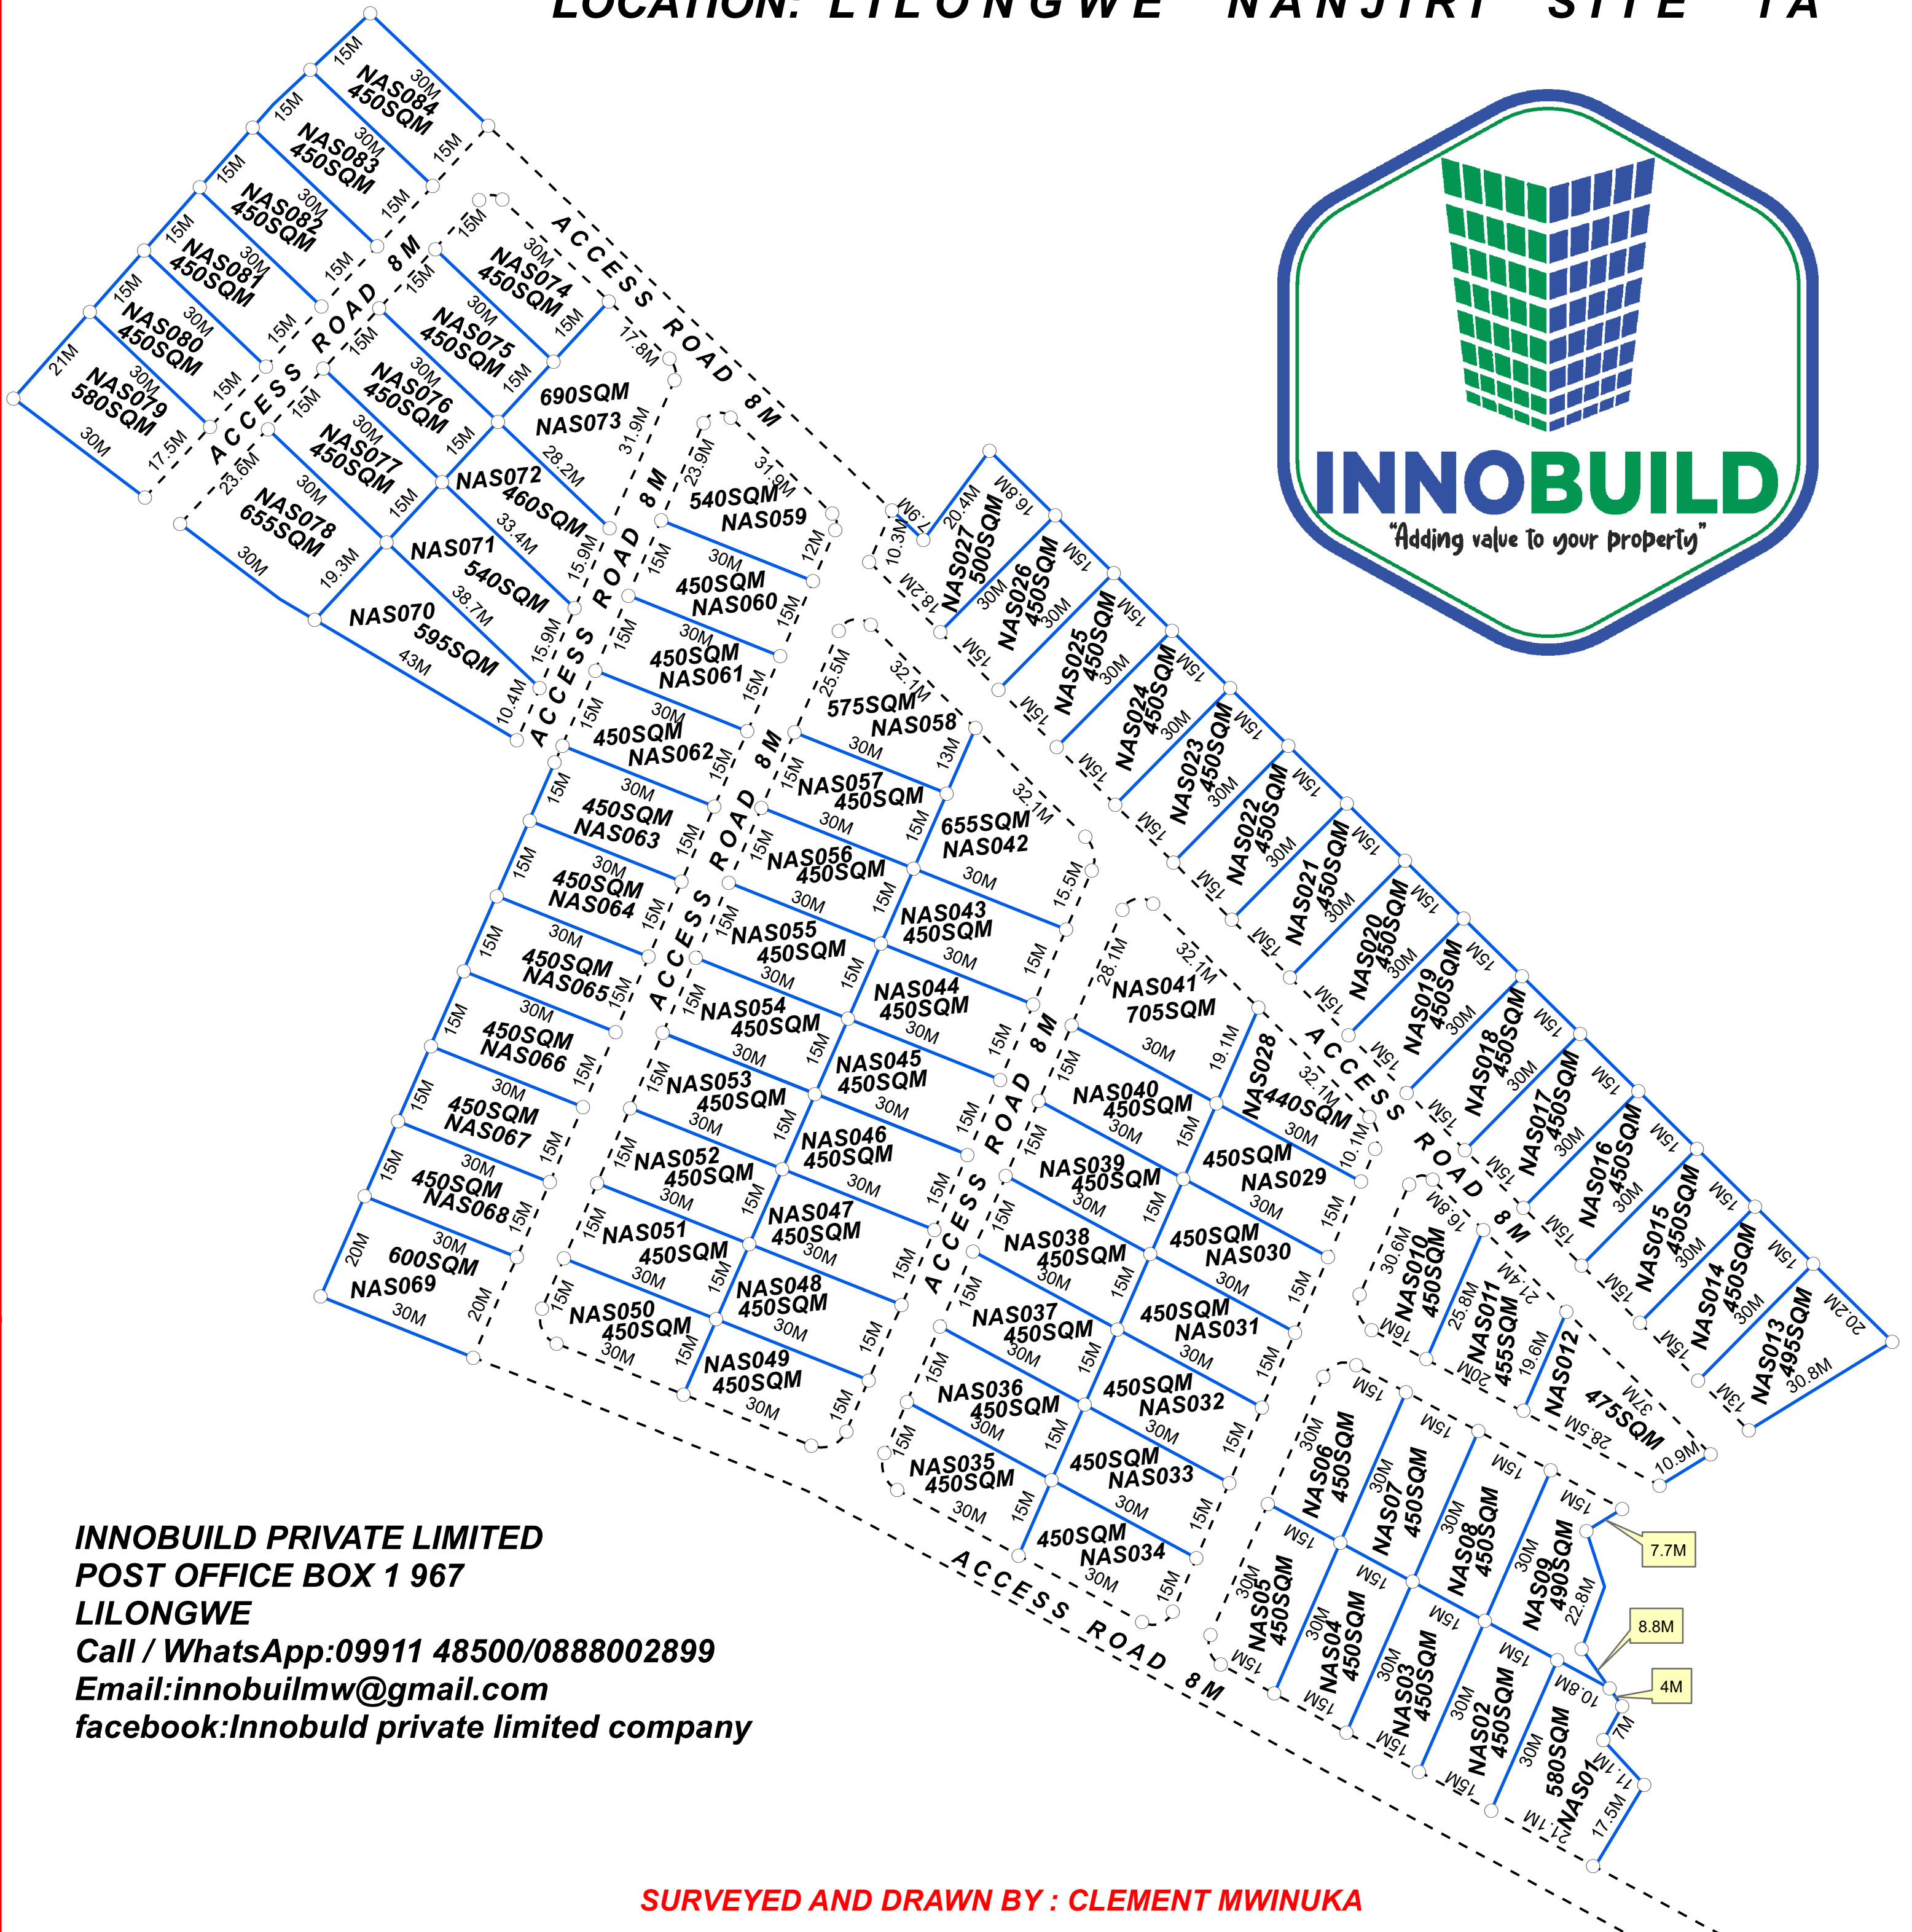

INNOBUILD PRIVATE LIMITED
POST OFFICE BOX 1 967
LILONGWE
Call / WhatsApp:09911 48500/0888002899
Email:innobuildmw@gmail.com
facebook:Innobuild private limited company

SURVEYED AND DRAWN BY : CLEMENT MWINUKA

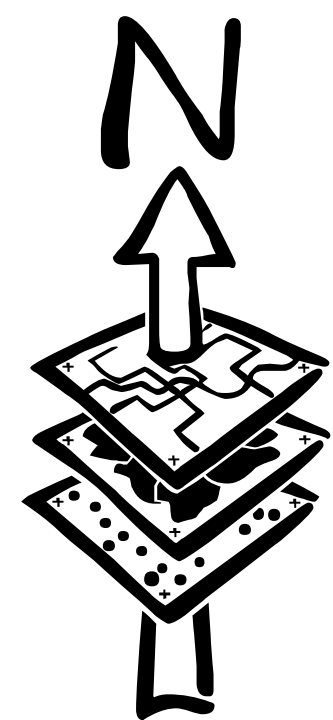

SCALE:1:850

