



LOCATION: LILONGWE CHINTEZE SITE 1

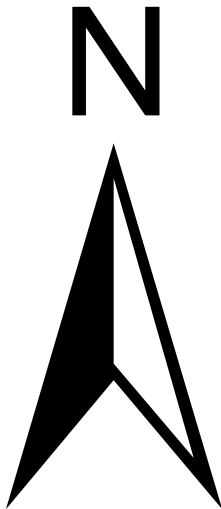

INNOBUILD PRIVATE LIMITED
POST OFFICE BOX 1 967
LILONGWE
Call / WhatsApp:09911 48500/0888002899
Email:innobuildmw@gmail.com
facebook:Innobuild private limited company

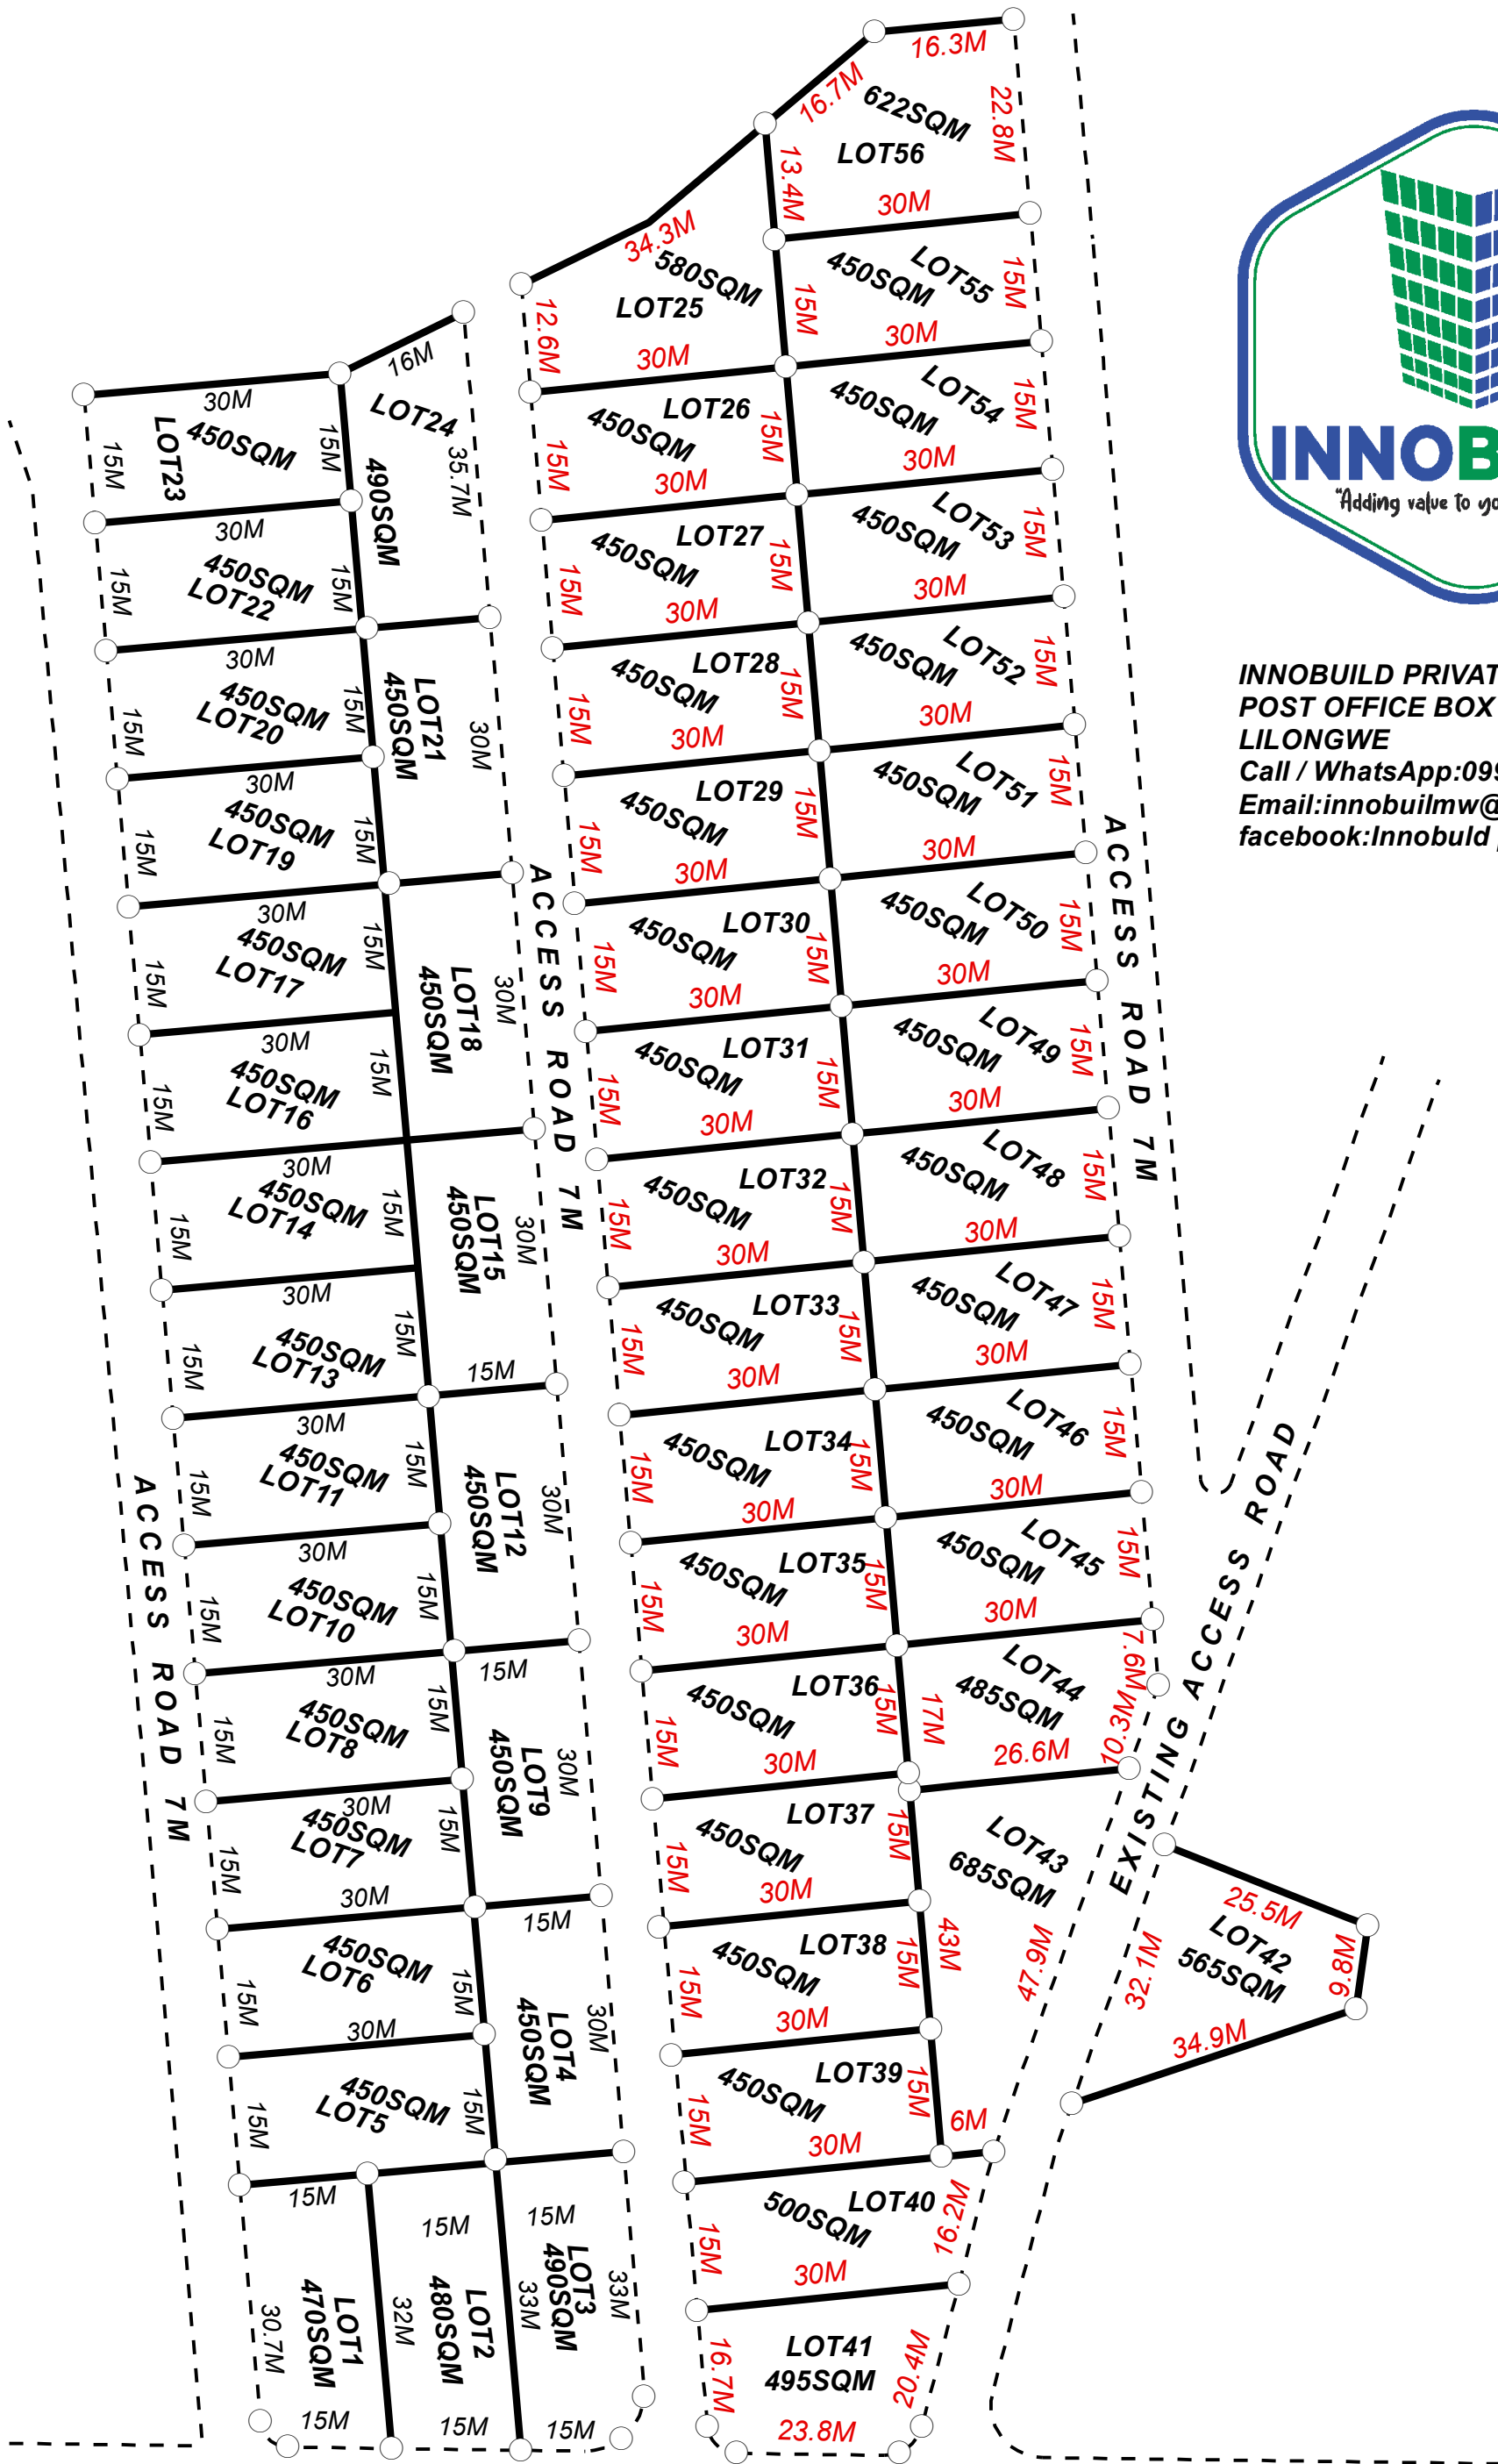

SCALE : 800