



LOCATION: LILONGWE NANJIRI SITE 1A

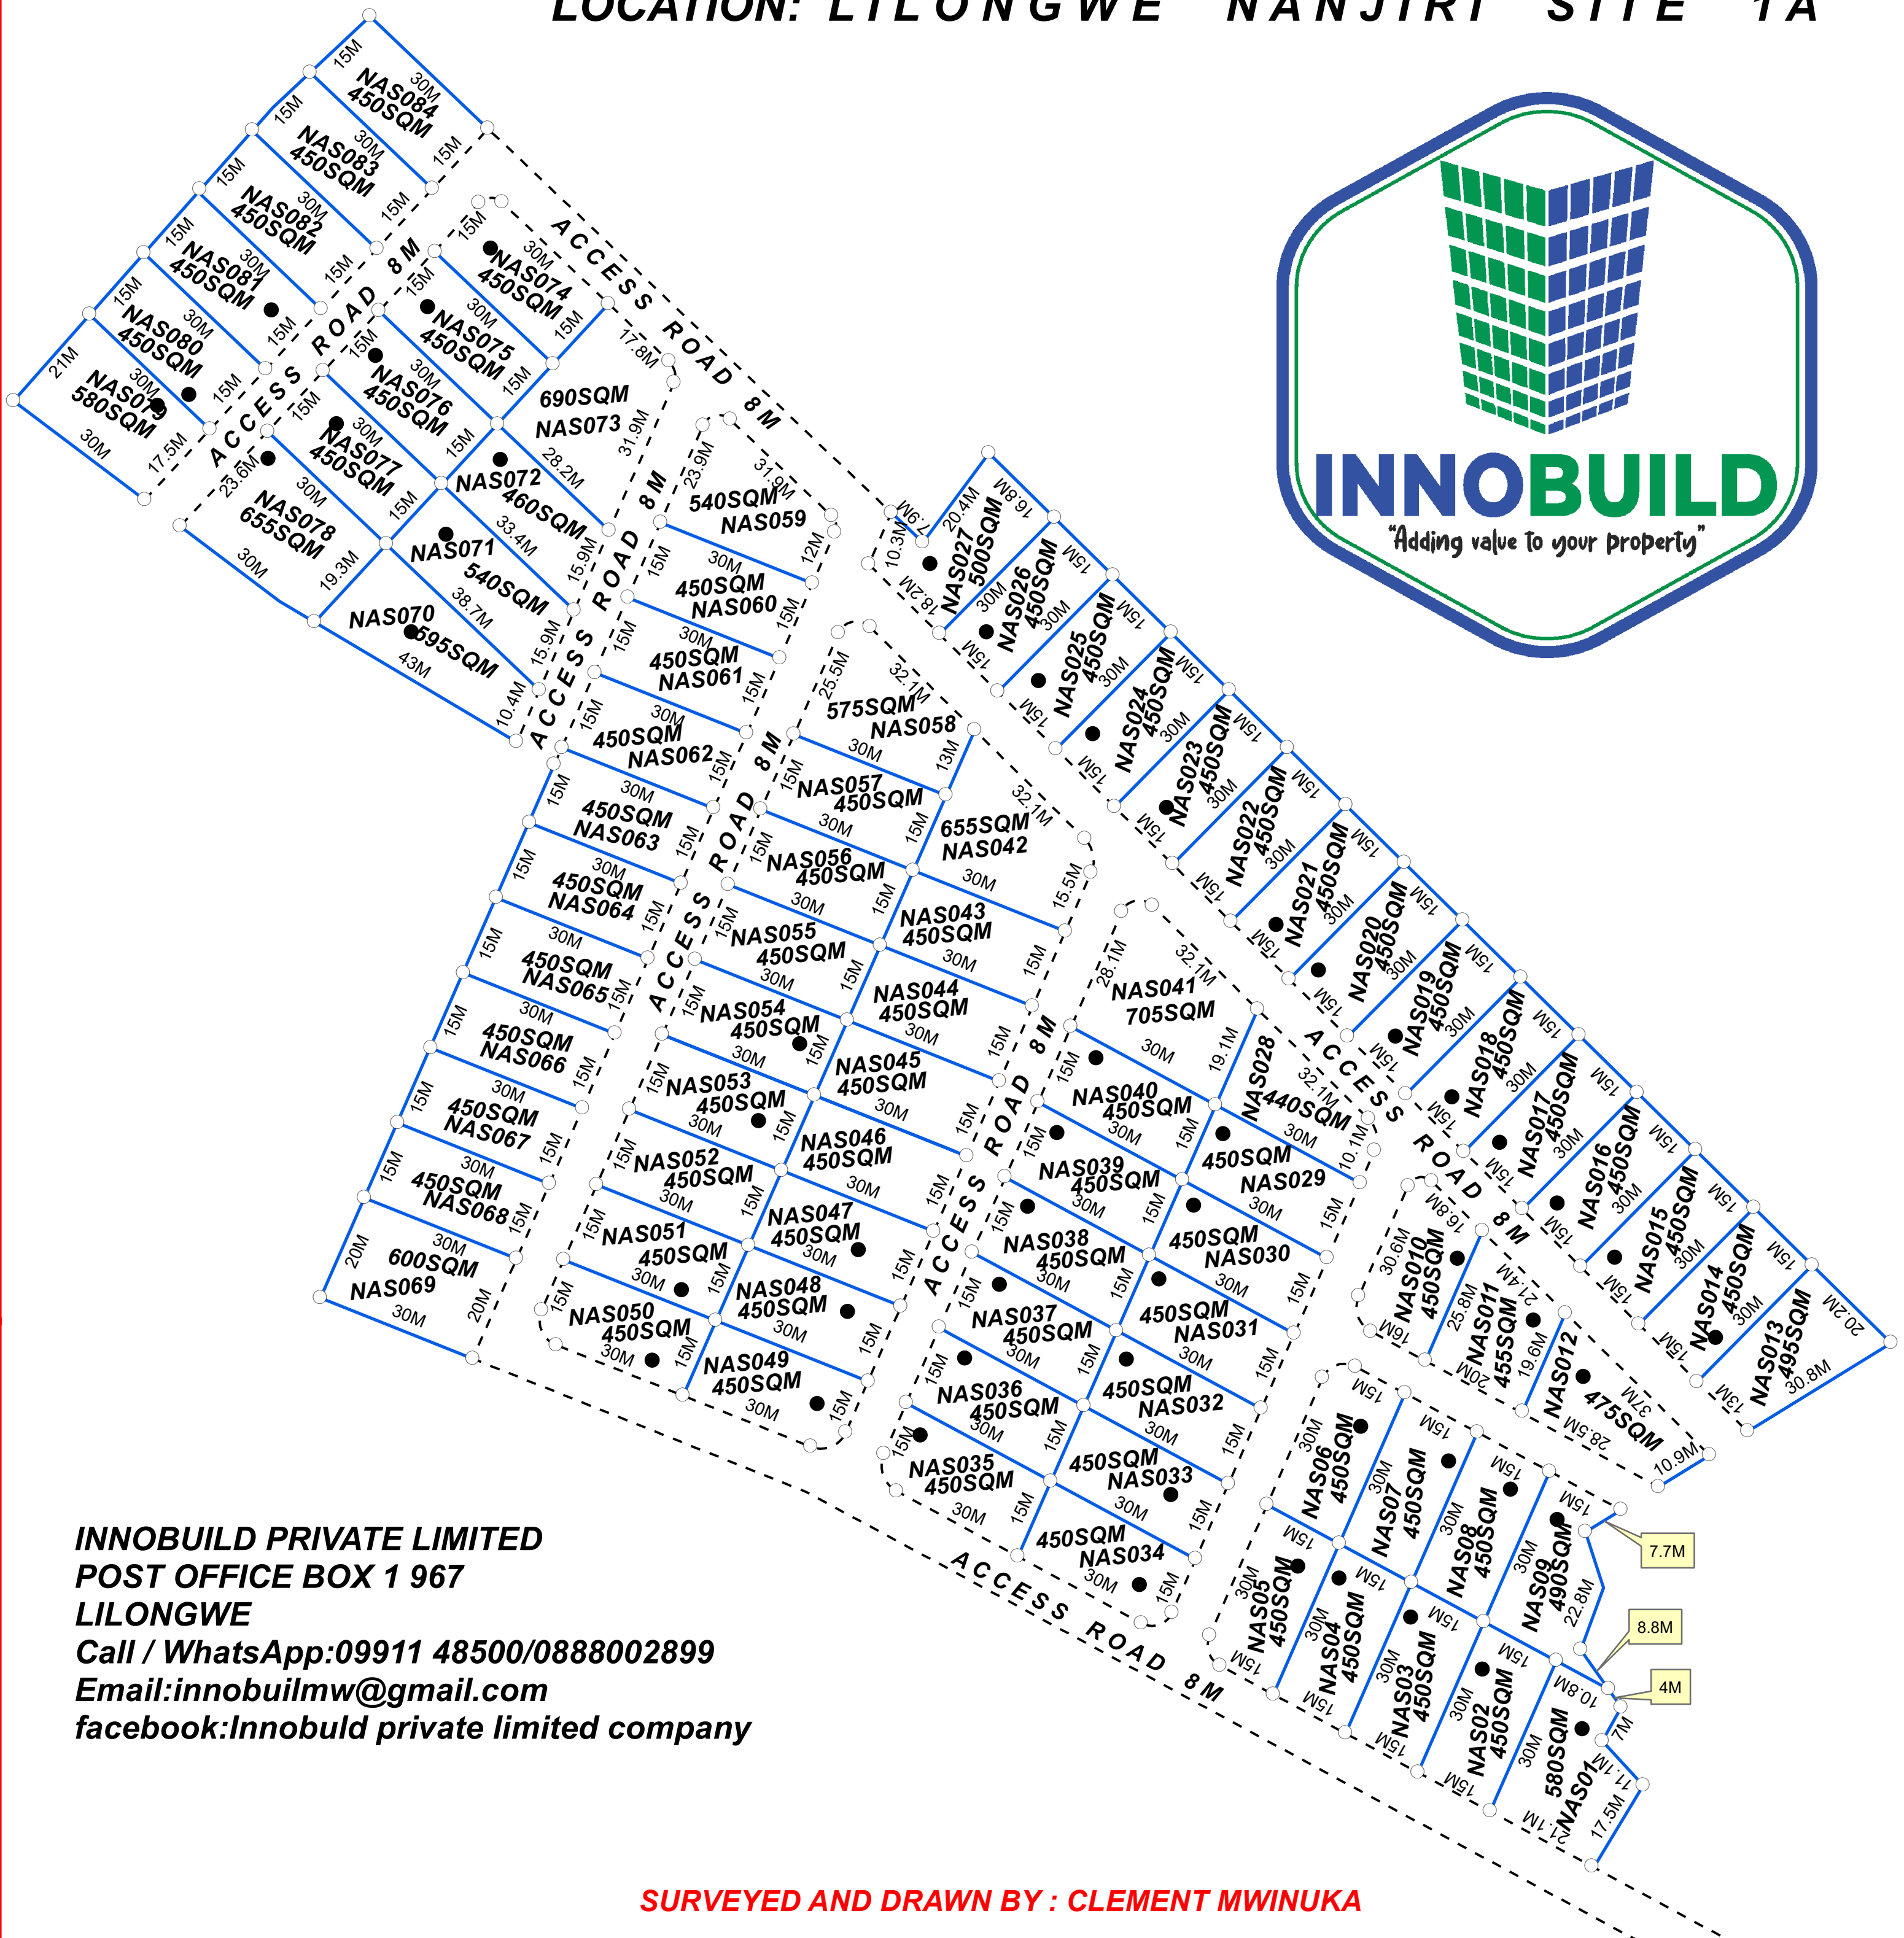

INNOBUILD PRIVATE LIMITED
POST OFFICE BOX 1 967
LILONGWE
Call / WhatsApp: 09911 48500/0888002899
Email: innobuildmw@gmail.com
facebook: Innobuild private limited company

SURVEYED AND DRAWN BY : CLEMENT MWINUKA

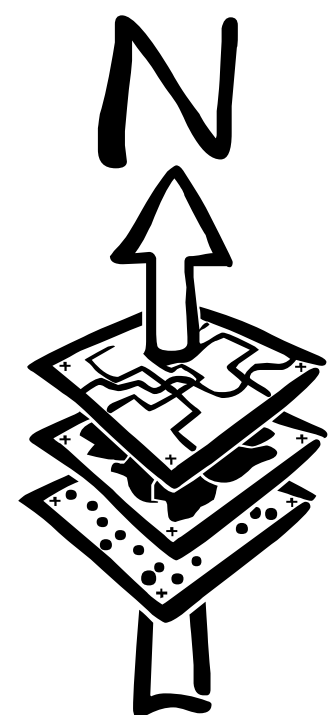

SCALE: 1:850

